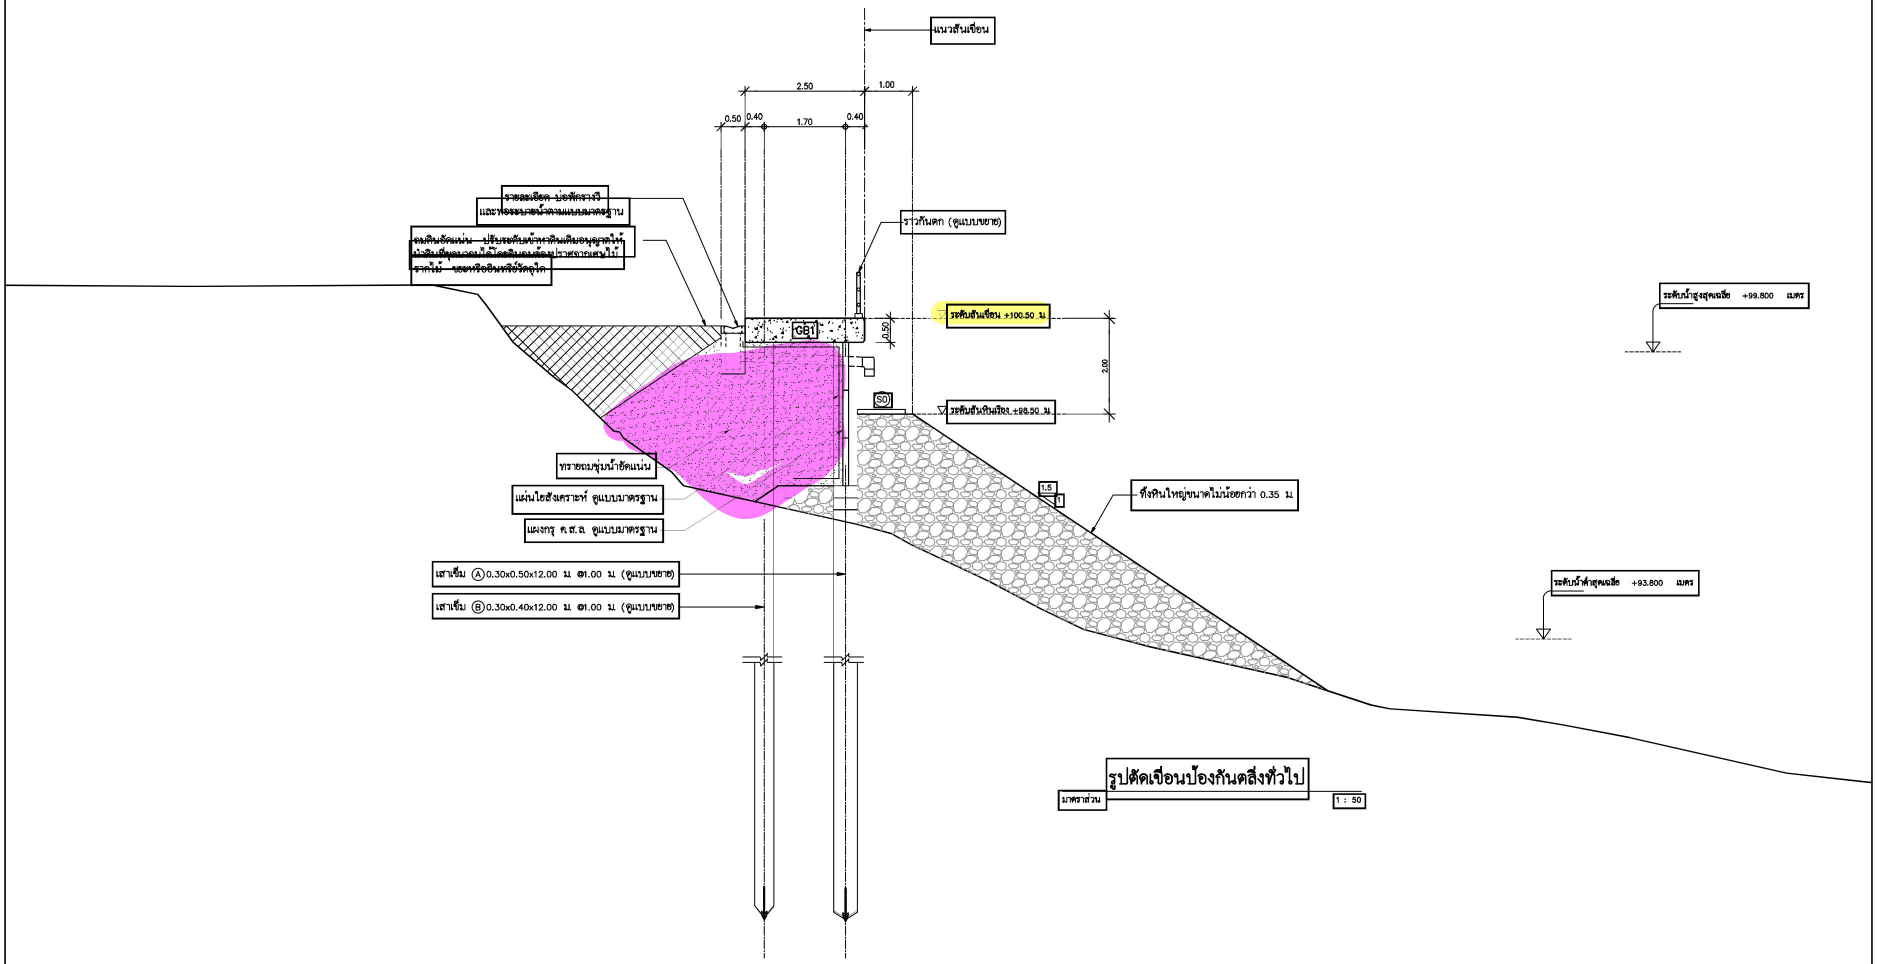
แนวสันเขื่อน
2.50
1.00
0.50
0.40
1.70
0.40
รายละเอียด บ่อพักรางวี และท่อระบายน้ำตามแบบมาตรฐาน
ถมดินอัดแน่น ปรับระดับเข้าหาดินเดิมอนุญาตให้นำดินที่ขุดมาถมได้โดยดินถมต้องปราศจากเศษไม้ รากไม้ ขยะหรืออินทรีย์วัตถุใดๆ
ราวกันตก (ดูแบบขยาย)
GB1
0.50
S0
ระดับสันเขื่อน +100.50 ม.
ระดับสันหินเรียง +98.50 ม.
2.00
1.5
1
ทิ้งหินใหญ่ขนาดไม่น้อยกว่า 0.35 ม.
ทรายถมชุ่มน้ำอัดแน่น
แผ่นใยสังเคราะห์ ดูแบบมาตรฐาน
แผงกรุ ค.ส.ล. ดูแบบมาตรฐาน
เสาเข็ม Ⓐ 0.30x0.50x12.00 ม. @1.00 ม. (ดูแบบขยาย)
เสาเข็ม Ⓑ 0.30x0.40x12.00 ม. @1.00 ม. (ดูแบบขยาย)
ระดับน้ำสูงสุดเฉลี่ย +99.800 เมตร
ระดับน้ำต่ำสุดเฉลี่ย +93.800 เมตร

รูปตัดเขื่อนป้องกันตลิ่งทั่วไป

มาตราส่วน 1 : 50

หมายเหตุ

1. มิติต่างๆเป็นเมตรและระดับสมมุติเป็นเมตร นอกจากระบุเป็นอย่างอื่น
2. ในกรณีที่พบว่าดินหินที่วางอยู่บนชั้นดินดาน หรือชั้นหินแข็ง ไม่สามารถก่อสร้างได้ตามแบบ ให้ผู้รับจ้างเสนอแบบแก้ไขต่อคณะกรรมการตรวจรับพัสดุ เพื่ออนุมัติก่อนดำเนินการก่อสร้าง

กรมโยธาธิการและผังเมือง

สำนักสนับสนุนและพัฒนาตามผังเมือง

กลุ่มงานศึกษาและออกแบบ

แบบ

เขื่อนป้องกันตลิ่งริมแม่น้ำฮี้
หมู่ที่ ๙ ตำบลป่งไฮ
อำเภอเซกา จังหวัดบึงกาฬ

แสดงแบบ

รูปตัดเขื่อนป้องกันตลิ่งทั่วไป

เลขที่แบบ	แผ่นที่	จำนวนแผ่น	วัน เดือน ปี	ใช้แทนแผ่นที่	เลขที่เก็บแบบ
D670257-47	47	65			

สำรวจ
เขียนแบบ
ออกแบบ
ตรวจ

ช่างสำรวจ
ช่างเขียนแบบ
วิศวกรโยธา
วิศวกรโยธา
วิศวกรโยธา

ตรวจ
หัวหน้ากลุ่มงานศึกษาและออกแบบ

ผ่าน
วิศวกรโยธาเชี่ยวชาญ

เห็นชอบ
ผู้อำนวยการสำนัก

อนุมัติ
(นาย)
อธิบดี