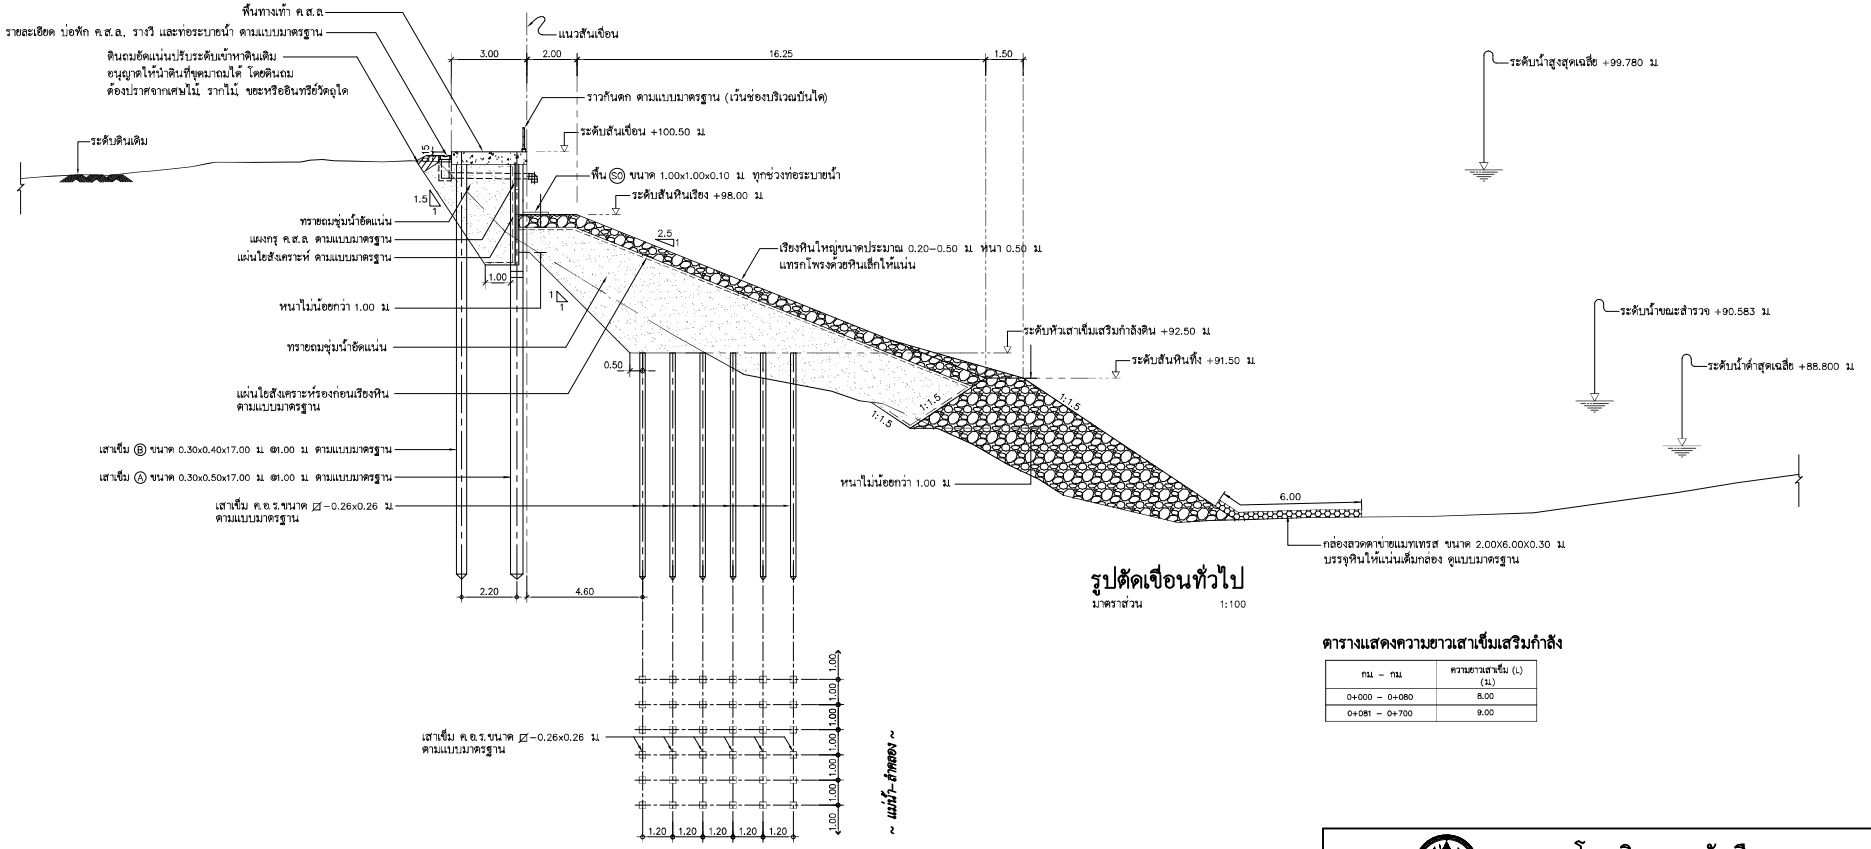


รูปตัดเขื่อนทั่วไป

มาตราส่วน 1:100

แปลนเสาเข็มเสริมกำลังดิน

มาตราส่วน 1:100

ตารางแสดงความยาวเสาเข็มเสริมกำลัง

กม. - กม.	ความยาวเสาเข็ม (L) (ม.)
0+000 - 0+080	8.00
0+081 - 0+700	9.00

หมายเหตุ

1. มิติต่างๆ เป็นเมตรและระดับสมมุติเป็นเมตร นอกจากระบุเป็นอย่างอื่น
2. ในกรณีที่พบว่าตันหินทิ้งวางอยู่บนชั้นดินดาน หรือชั้นหินแข็ง ไม่สามารถก่อสร้างได้ตามแบบ ให้ผู้รับจ้างเสนอแบบแก้ไข ต่อคณะกรรมการตรวจรับพัสดุ เพื่ออนุมัติก่อนดำเนินการก่อสร้าง

ครั้งที่	รายการแก้ไข	วันที่	
1			
2			
3			
4			
5			
6			

กรมโยธาธิการและผังเมือง
สำนักสนับสนุนและพัฒนาตามผังเมือง

โครงการก่อสร้างเขื่อนป้องกันตลิ่งริมแม่น้ำภายในประเทศ

แก้ไขสัญญา ครั้งที่ 2
เขื่อนป้องกันตลิ่งริมแม่น้ำน่าน หมู่ที่ 5
ตำบลโคกสลุด อำเภอบางกระทุ่ม จังหวัดพิษณุโลก

รูปตัดเขื่อนทั่วไป

วิศวกรออกแบบ : นายรัฐธรรม อิสโรพาร สย.เลขที่ 2349
เขียนแบบ : นายเทพเทวัญชัย สิงห์ประเสริฐ
ตรวจ : นายเพิ่มพร ศรีโรบล วย.2349
ผู้จัดการโครงการ : นายมนตรี ต้นตระกูล วย.1205
วันที่ :

บริษัท วี เอส พี เอส เอ็นจิเนียริ่ง จำกัด
บริษัท พร็อนเทียร์ เอ็นจิเนียริ่ง คอนซัลแทนท์ส จำกัด
บริษัท ไทยดอนซัลแตนท์ เอ็นจิเนียริ่ง จำกัด

แผ่นที่แบบ	แผ่นที่	จำนวนแผ่น
NAN2-V06-SD-01R1	23	48