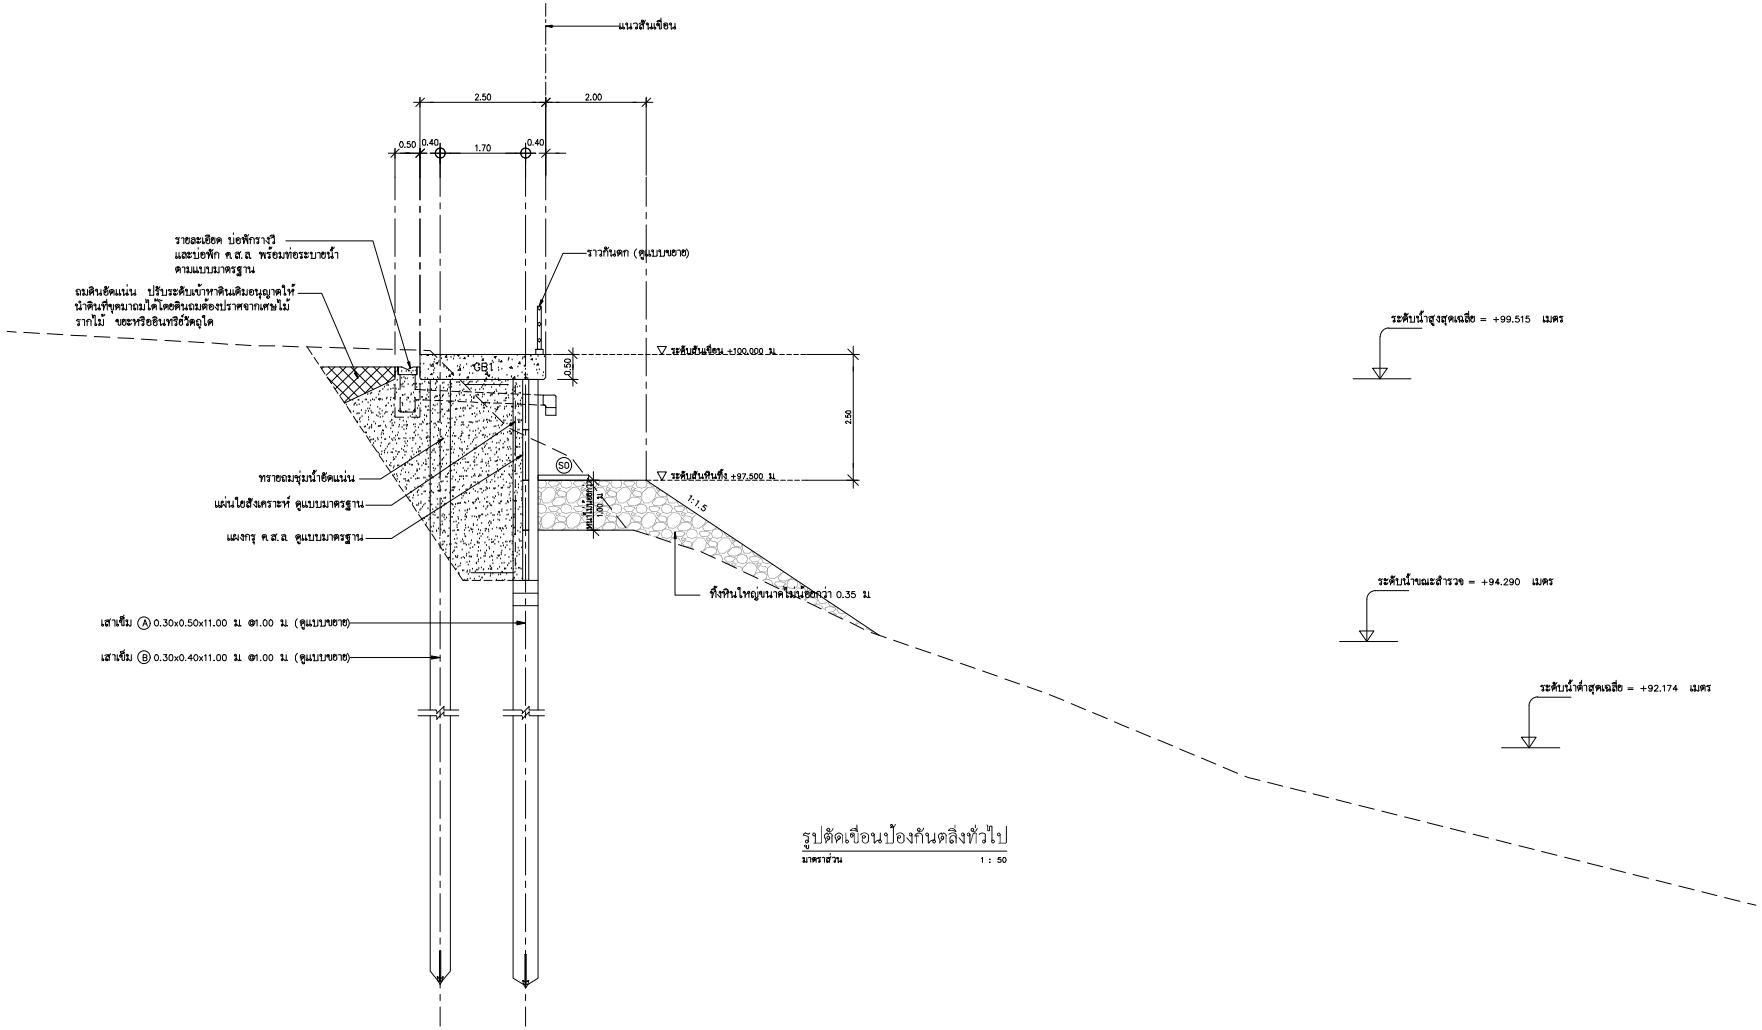


รูปตัดเขื่อนป้องกันตลิ่งทั่วไป

มาตราส่วน 1 : 50

หมายเหตุ

1. มิติต่างๆเป็นเมตรและระดับรมมุลเป็นเมตร นอกจากระบุเป็นอย่างอื่น
2. ในกรณีที่พบว่าดินที่วางอยู่บนชั้นดินดาน หรือชั้นหินแข็ง ไม่สามารถก่อสร้างได้ตามแบบ ให้ผู้รับจ้างเสนอแบบแก้ไขต่อคณะกรรมการตรวจรับพัสดุ เพื่ออนุมัติก่อนดำเนินการก่อสร้าง
3. กำหนดให้ผู้รับจ้างใช้นิ้วร้อนในการตอกเสาเข็มโครงสร้างเขื่อนป้องกันตลิ่ง ทั้งนี้ผู้รับจ้างสามารถใช้วิธีการตอกเสาเข็มรูปแบบอื่นที่แตกต่างไปจากที่กำหนดได้ โดยต้องเสนอแนวทางและวิธีการทำงานเพื่อการเปรียบเทียบราคา พร้อมวิศวกรเซนต์รับรองเพื่อขออนุมัติก่อนเริ่มดำเนินการก่อสร้าง

ครั้งที่	รายการแก้ไข	วันที่	ตรวจ
1			
2			
3			
4			
5			
6			

กรมโยธาธิการและผังเมือง
สำนักสนับสนุนและพัฒนาตามผังเมือง

โครงการก่อสร้างเขื่อนป้องกันตลิ่งริมแม่น้ำภายในประเทศ

เขื่อนป้องกันตลิ่งริมแม่น้ำปราจีนบุรี
หมู่ที่ 4 บ้านบึงทาพี
ตำบลหาดนางแก้ว อำเภอกบินทร์บุรี จังหวัดปราจีนบุรี

รูปตัดเขื่อนป้องกันตลิ่งทั่วไป

บริษัท ซีพีเอส ซัคเซส จำกัด
บริษัท เอส ที เอส เอ็นจิเนียริ่ง คอนซัลแตนท์ จำกัด
บริษัท บุญบัญญา เทคโนโลยี จำกัด

วิศวกรออกแบบ : ชื่อ ณรงค์ฤทธิ์ อุปพลเมียร สย.10301
เขียนแบบ : ชื่อ ศุภเดช เพิ่มศรี ภย.88910
ชื่อ อนันตพล มายุติริ ภย.85312
ชื่อ อรสา ละอิว ภย.74070
ตรวจ : ชื่อ ณรงค์ฤทธิ์ อุปพลเมียร สย.10301
ผู้จัดการโครงการ :
วันที่ :

เลขที่แบบ	แผ่นที่	จำนวนแผ่น
68-PR03-SD-01	39	61